
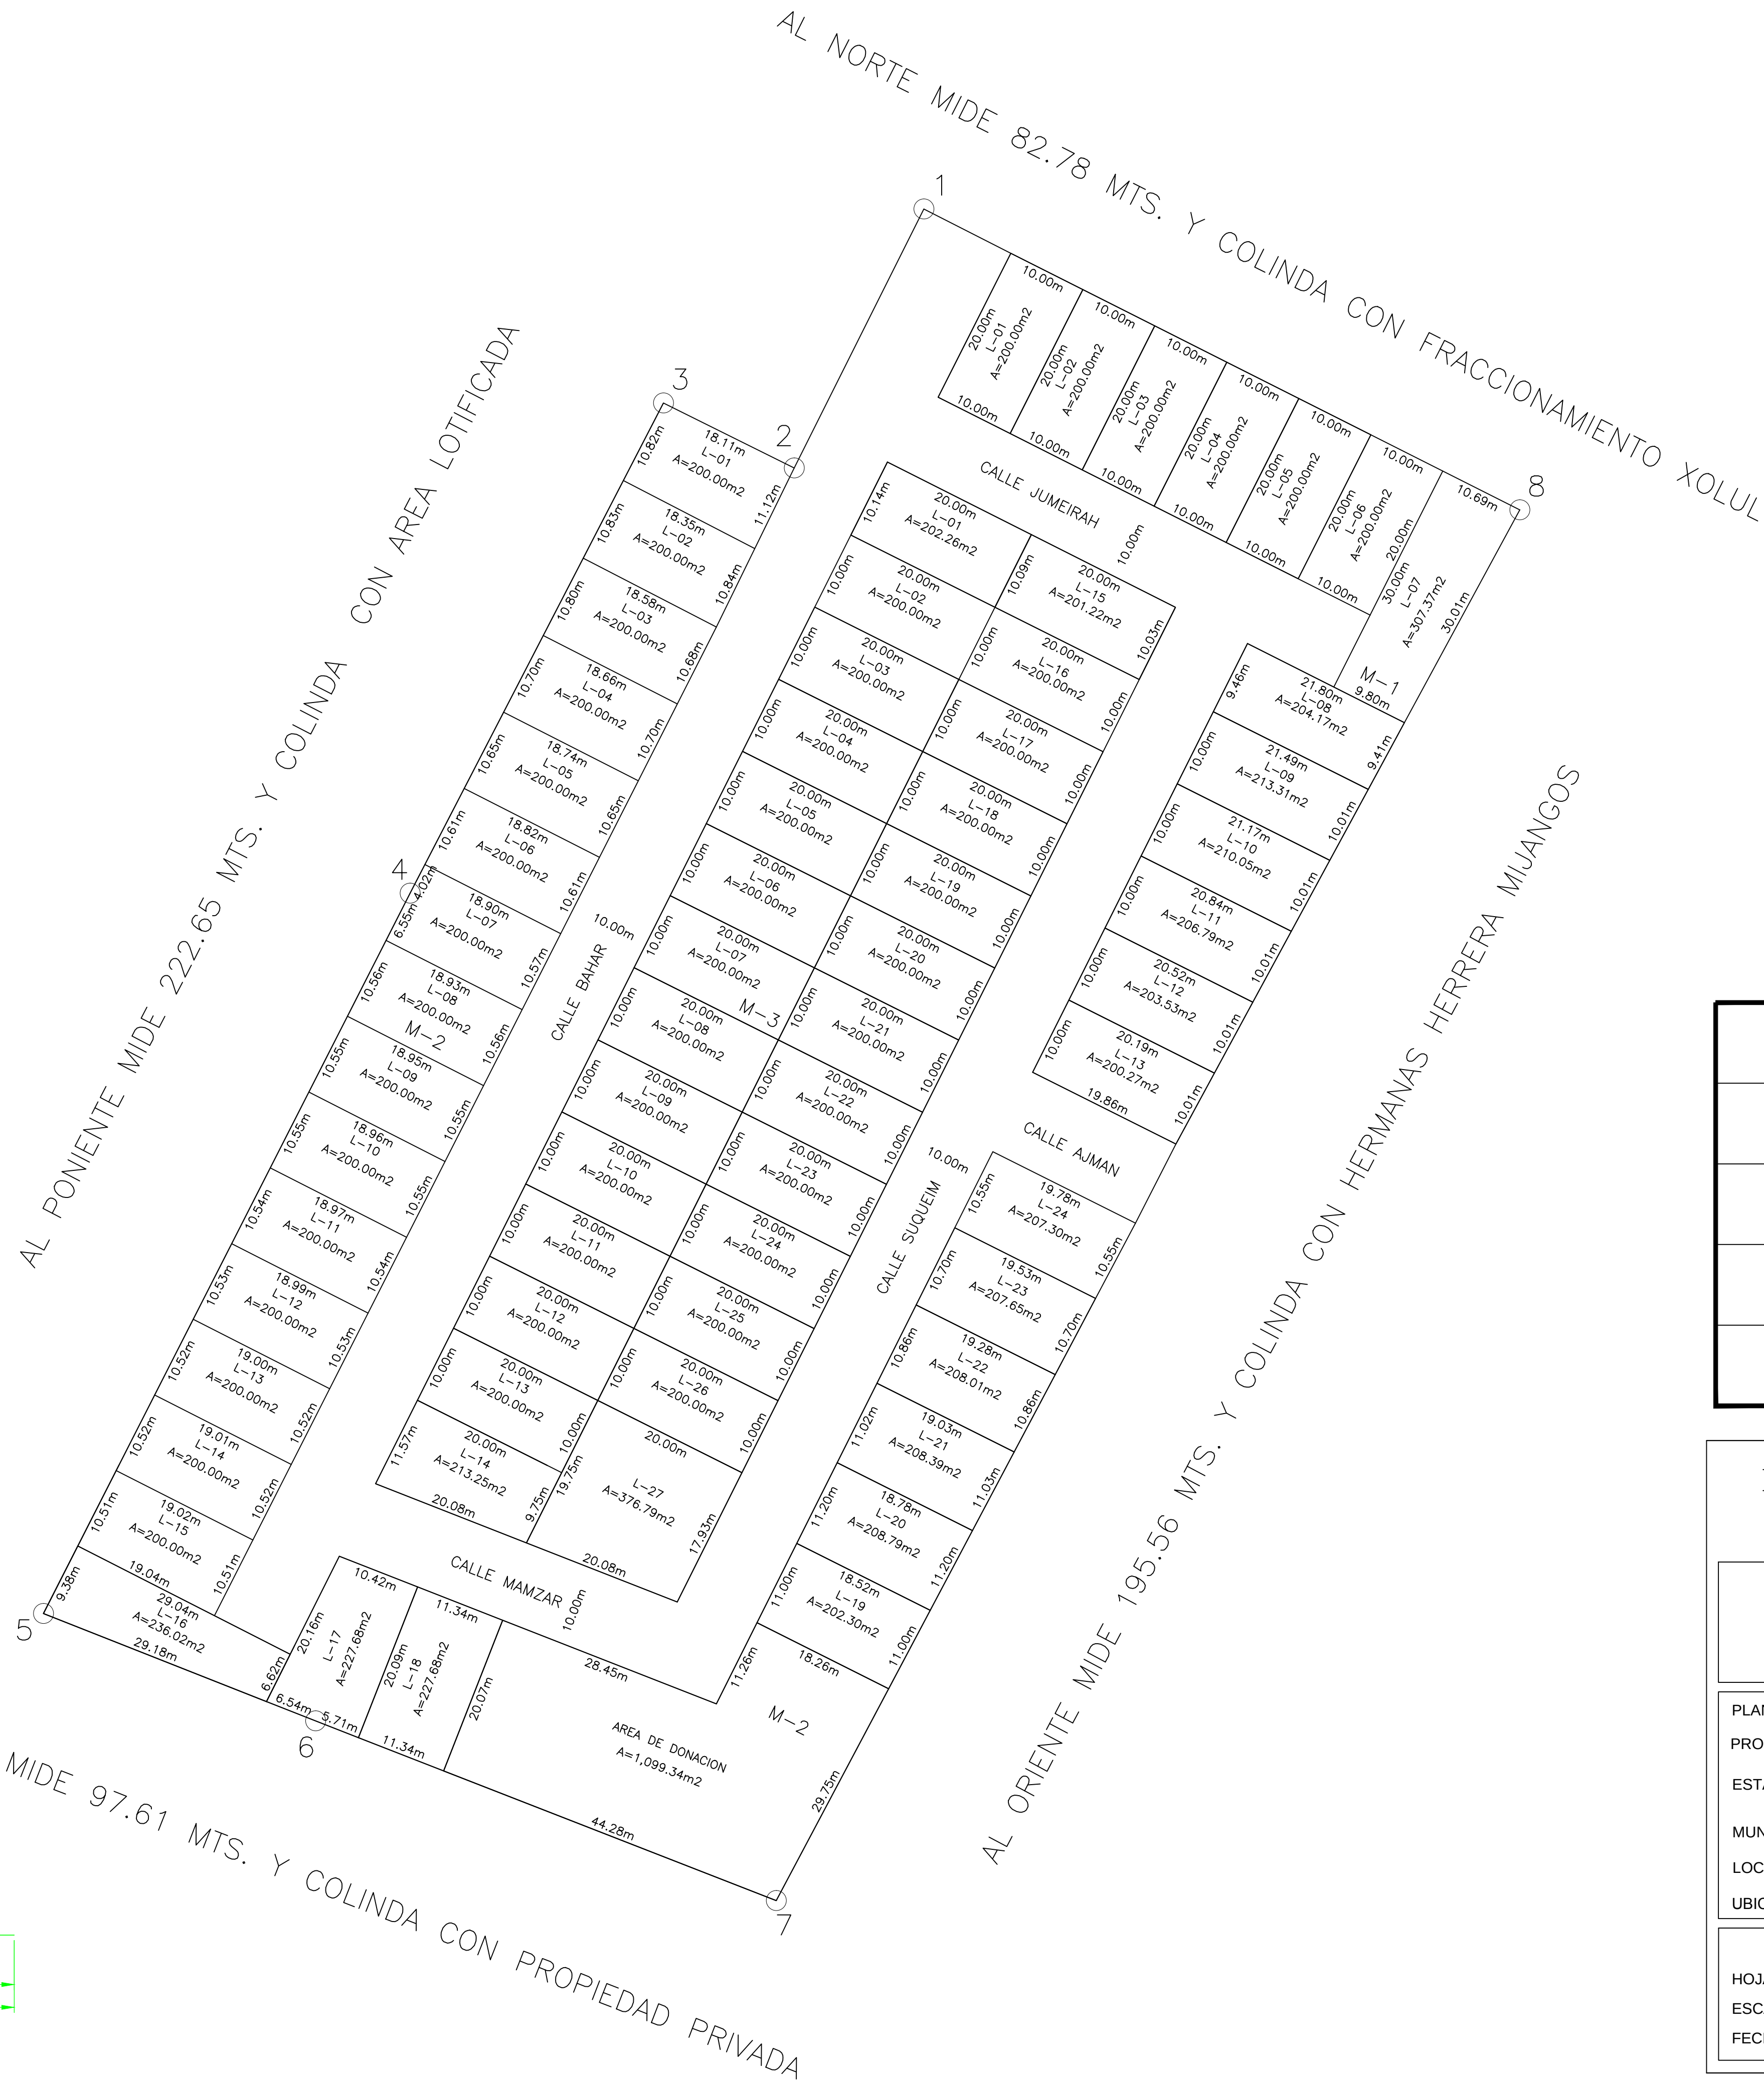


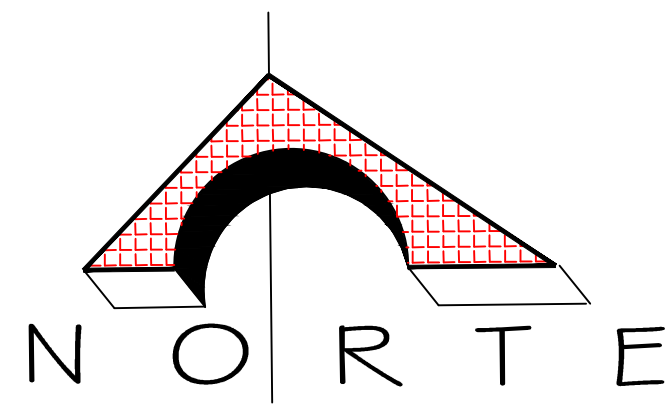

CUADRO DE AREAS	
AREA LOTIFICADA	13,306.38 m2
AREA DE CALLE	4,750.11 m2
AREA DE DONACION	1,093.34 m2
AREA TOTAL	19,149.83 m2

PROYECTO:

LEVANTAMIENTO TOPOGRAFICO

RESPONSABLE DEL LEVANTAMIENTO:

TOPOGRAFIA DE LA COSTA S.C.

PLANO DE:

LOTIFICACION

PROPIETARIO:

C. HERMANAS HERRERA MIJANGOS

ESTADO:

OAXACA

MUNICIPIO:

SANTA MARIA COLOTEPEC

LOCALIDAD:

EL ROSEDAL

UBICACIÓN:

SHAYBAH RESIDENCIAL

SIMBOLOGIA

VERTICE DE POLIGONO

LINEA DE POLIGONO

CERCA DE ALAMBRE

VIALIDAD

ARROYO

LOTE

N° DE LOTE

MANZANA -1

HOJA:

1 DE 1

ESCALA:

1:500

FECHA:

MARZO DE 2024