




RESIDENCIAL YIVANA


NORTE



CUADRO DE AREAS		
AREA TOTAL DE POLIGONO	A= 103,700.98 M2	
MANZANAS	LOTES	AREA
AREA DE M-1	1	A= 303.97 m2
AREA DE M-2	14	A=17,116.81 m2
AREA DE M-3	11	A=3,005.13 m2
AREA DE M-4	3	A=1,249.34 m2
AREA DE M-5	15	A=4,727.13 m2
AREA DE M-6	5	A=4,349.28 m2
AREA DE M-7	4	A=2,491.57 m2
AREA DE M-8	4	A=1,579.86 m2
AREA DE M-9	4	A=2,563.53 m2
AREA DE M-10	10	A=5,655.22 m2
AREA DE M-11	8	A=3,452.54 m2
AREA DE M-12	8	A=2,587.32 m2
AREA DE M-13	8	A=1,844.40 m2
AREA DE M-14	4	A= 826.47 m2
AREA DE M-15	20	A=5,777.42 m2
AREA DE M-16	19	A=4,380.94 m2
AREA DE M-17	15	A=3,439.40 m2
AREA DE M-18	14	A=2,968.80 m2
	167	
AREA VENDIBLE	A= 68,319.12 M2	
AREA DE DONACION	A= 6,831.91 M2	
AREA DE VIALIDAD	A= 28,549.95 M2	

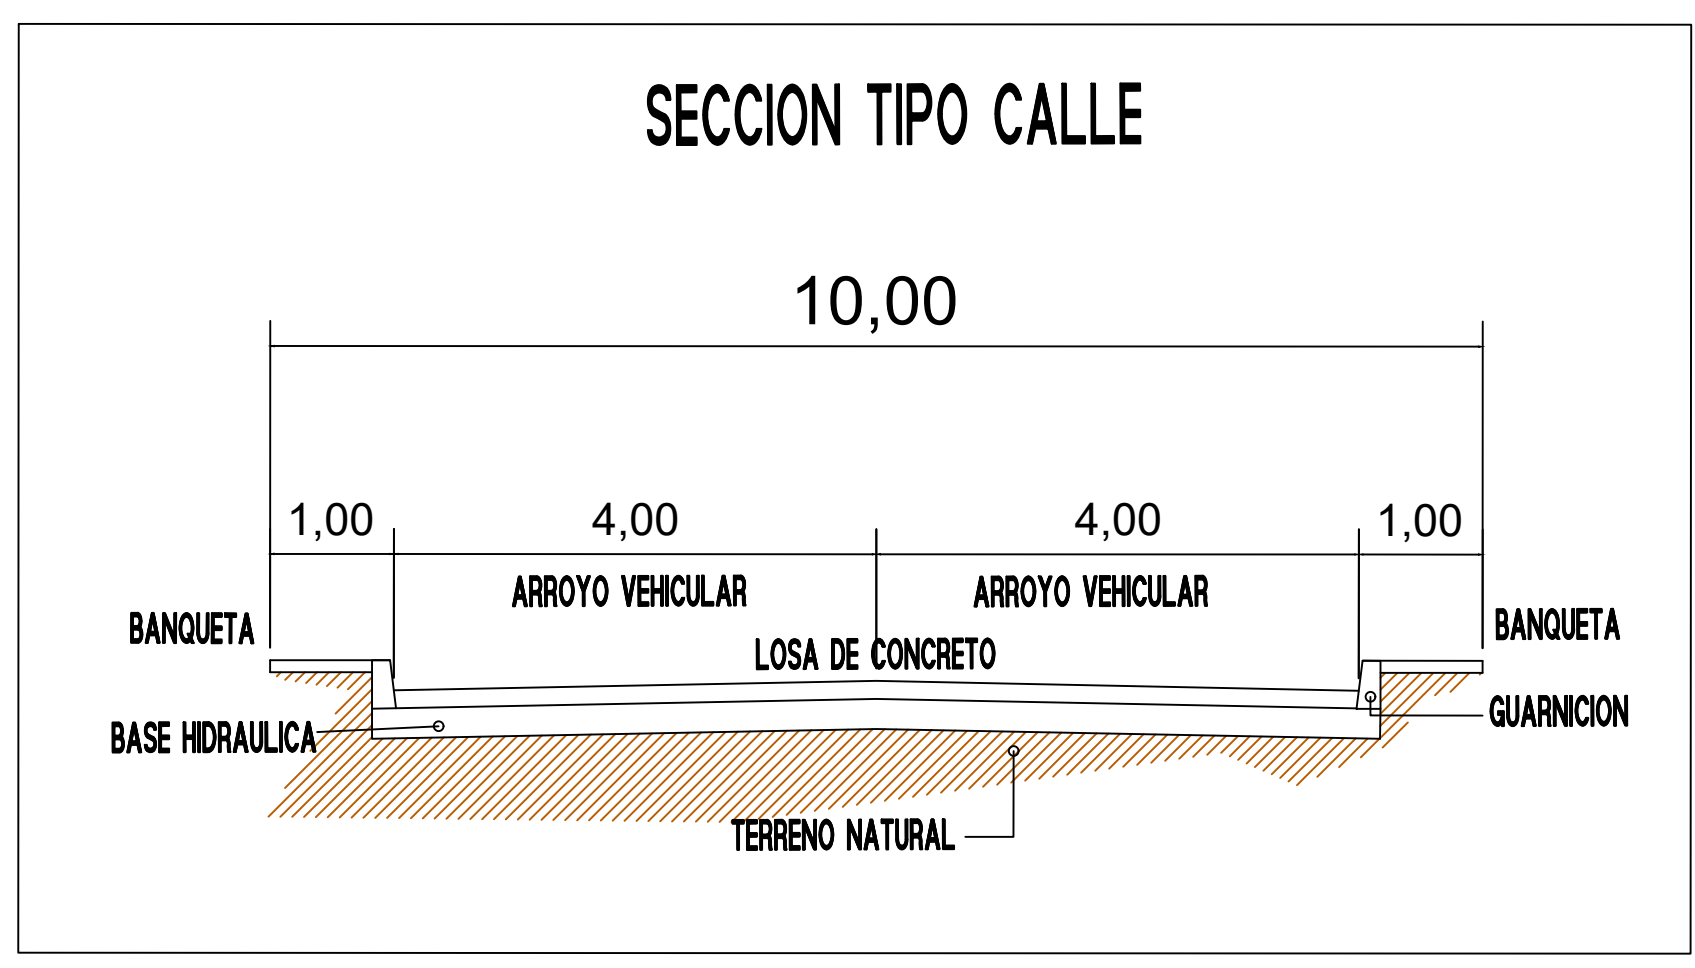

CONSTRUCCIONES TRISGO & ASOCIADOS
S.A. DE C.V.
CELULAR 9541227085

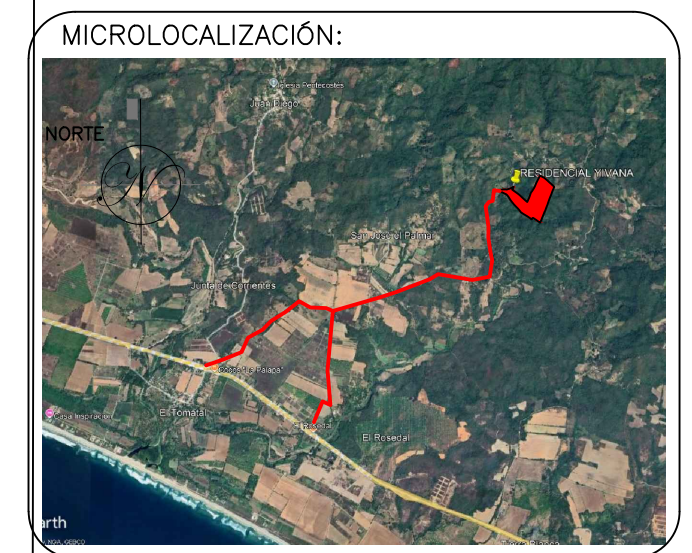

FIRMA Y SELLO

DATOS GENERALES
UBICACION: ARROYO TOMATAL
LOCALIDAD: EL TOMATAL
MUNICIPIO: SANTA MARIA COLOTEPEC
ESTADO: OAXACA
PLANO: LOTIFICACION
PROYECTO: ING. AGUSTIN VICTORINO TRISTE GONZALEZ
D.R.ING. AGUSTIN VICTORINO TRISTE GONZALEZ
CED.PRO.: 9545847 DRO.: A-0015-I SMC

SE LEVANTO CON ESTACION TOTAL MARCA TOPCOM
MODELO GOWIN CON PRECISION DIGITAL.
LAS MEDIDAS FUERON LEVANTADAS FISICAMENTE EN EL
LUGAR RESPETANDO CERCAS EXISTENTES Y COLINDANCIAS.
PROPIETARIO:
ANGELICA RUIZ VALENCIA

CLAVE LOT-SUB		No. PLANO 01-01
ESCALA S/E	FECHA JUNIO DEL 2026 COTAS mts	