


CUADRO DE RESUMEN DE AREAS	
AREA DE VIALIDADES	19,943.54 M2
AREA TOTAL VENDIBLE	60,267.80 M2
ÁREA DE DONACIÓN	6,026.65 M2
ÁREA DE SERVICIO	697.95 M2
AREA TOTAL GENERAL	86,935.94 M2

"FRACCIONAMIENTO MARELLA"

C. MATEO PACHECO
COLINDANTE NORTE
A-F=353.00m

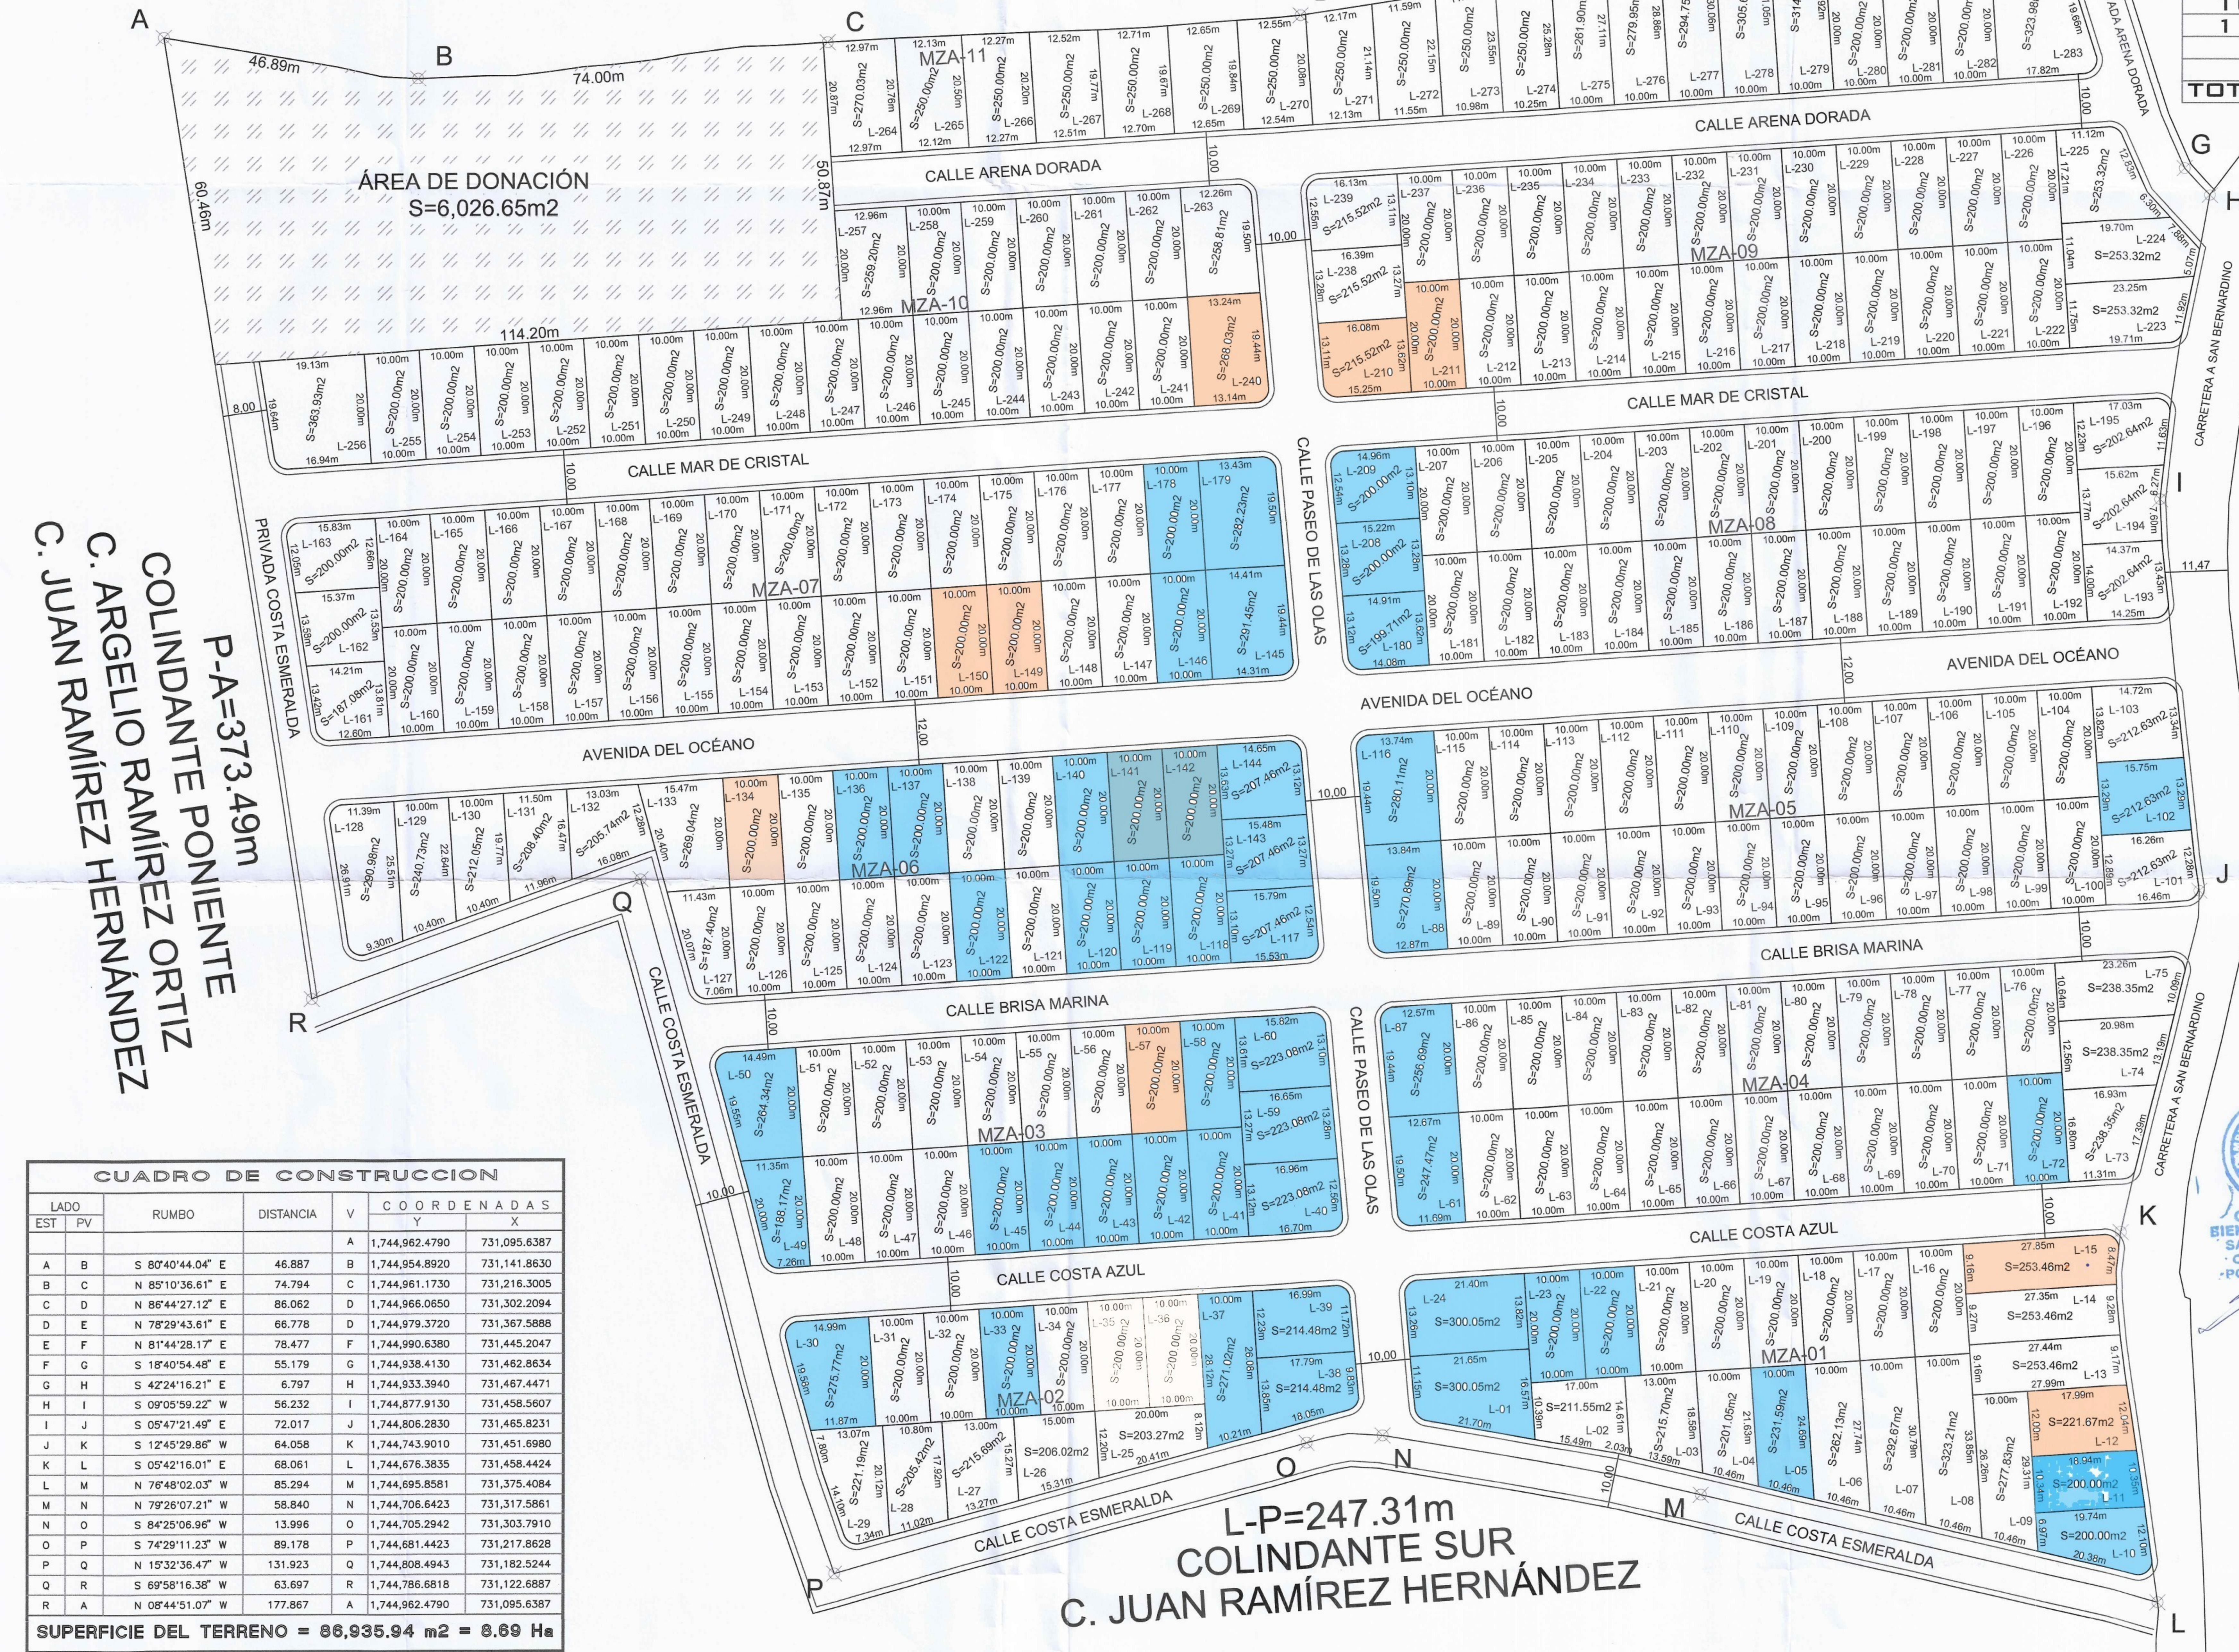


CUADRO DE AREAS		
NO. MZA	NO. LOTES	AREAS
01	24	5,597.88
02	15	3,227.34
03	21	4,321.75
04	27	5,619.21
05	29	5,988.89
06	28	5,836.72
07	35	7,160.76
08	30	6,007.63
09	30	6,206.52
10	24	5,149.97
11	20	5,151.13
TOTAL	283	60,267.80

● VENDIDO
● APARTADO

F-L=322.35m
COLINDANTE ORIENTE
CARRETERA A SAN BERNARDINO

LADO		RUMBO		DISTANCIA		COORDENADAS	
EST	PV					X	Y
A	B	S 80°40'44.04" E		46.887		1,744,962.4790	731,095.6387
B	C	N 85°10'36.61" E		74.794		1,744,954.8920	731,141.8630
C	D	N 86°44'27.12" E		86.062		1,744,966.0650	731,302.2094
D	E	N 78°29'43.61" E		66.778		1,744,979.3720	731,367.5888
E	F	N 81°44'28.17" E		78.477		1,744,990.6380	731,445.2047
F	G	S 18°40'54.48" E		55.179		1,744,938.4130	731,462.8634
G	H	S 42°21'16.21" E		6.797		1,744,933.3940	731,467.4471
H	I	S 09°05'59.22" W		56.232		1,744,877.9130	731,458.5807
I	J	S 05°47'21.49" E		72.017		1,744,806.2830	731,465.8231
J	K	S 12°45'29.86" W		64.058		1,744,743.9010	731,451.6980
K	L	S 05°42'16.01" E		68.061		1,744,676.3835	731,458.4424
L	M	N 76°48'02.03" W		85.294		1,744,695.8581	731,375.4084
M	N	N 79°26'07.21" W		58.840		1,744,706.6423	731,317.5861
N	O	S 84°25'06.96" W		13.996		1,744,705.2942	731,303.7910
O	P	S 74°29'11.23" W		89.178		1,744,681.4423	731,217.8628
P	Q	N 19°32'36.47" W		131.923		1,744,808.4943	731,182.5244
Q	R	S 69°58'16.38" W		63.697		1,744,786.6818	731,122.6887
R	A	N 08°44'51.07" W		177.867		1,744,962.4790	731,095.6387

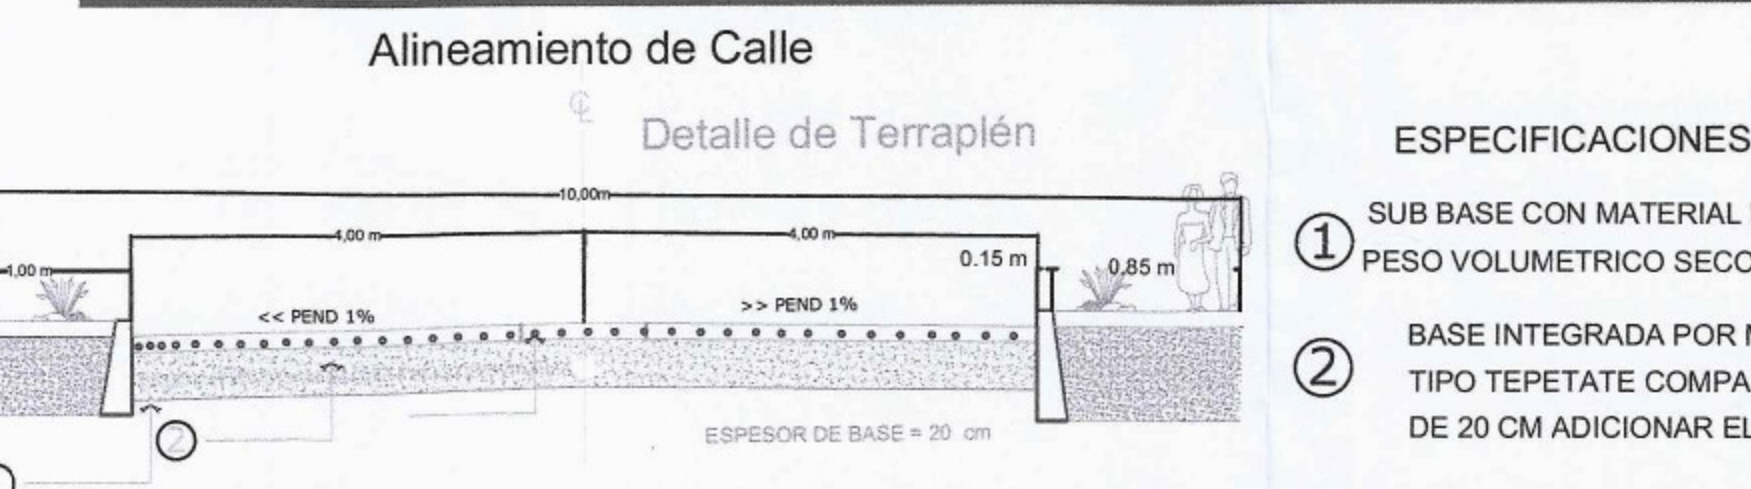

PROYECTO
"FRACCIONAMIENTO MARELLA"
CONTENIDO
* Subdivisión de predio.
* Especificaciones



DATOS GENERALES
● EL LEVANTAMIENTO SE REALIZO CON EQUIPO TOPOGRAFICO DE PRECISION DIGITAL. ESTACION TOTAL, MARCA TOPCON ES 55.
● SE ESTABLECIERON PUNTOS DE REFERENCIA (PINTURA DE COLOR ROJO) EN CADA DEFLEXION, A LO LARGO DE TODA LA COLINDANCIA Y PUNTOS DE CONTROL PARA REPERTE DE MEDIDAS.
● LAS MEDIDAS FUERON TOMADAS FISICAMENTE DEL LUGAR, RESPETANDO LOS CEROS DE LAS COLINDANCIAS.
● EL DIBUJO, COMO LOS CUADROS DE CONSTRUCCION, SE REALIZARON CON EL PROGRAMA CIVIL CAD.
● EL NORTE ES MAGNETICO
● LA COTA DADA EN METROS.
● LA COTA RISE AL DIBUJO.
● EL ANCHO DE LAS CALLES SERAN DE 10.00 M

NOMENCLATURA
Lindero del Predio
Calles de acceso

AUTORIZACION MUNICIPAL

PERITO RESPONSABLE DE OBRA
ING. SYNDEL SANCHEZ GUERRA.
CED. PROF.: 09182142 C-1
DRO. A-008-I SMC.
DRO. ESTATAL: B-4034-I

DATOS DEL PROYECTO

PROYECTO: "FRACCIONAMIENTO MARELLA"

PROPIETARIO: C. LAURA ALEJANDRA CORTES MONTAÑO.

PLANO: * Topografía
* Cuadro de Lotificación
* Cuadro de Áreas

UBICACION: CARRETERA A SAN BERNARDINO, LA CULEBRA, SAN FRANCISCO COZCOATEPEC, POCHUTLA, OAX.

CONSTRUCCION & TOPOGRAFIA DE LA COSTA

LEVANTO, DIB. Y PROJ.:
ING. SYNDEL SANCHEZ GUERRA.
CED. PROF.: 09182142 C-1

NOMBRE DE PLANO:
LOTIFICACION

ACOT: METROS ESC: 1:650

FECHA: ABRIL 2025 PLANO Nº: LOT-01